

İCRAÇI "PROJE44" MMC
SİFARİŞÇİ ABBASOVA ƏFSANƏ ŞAMİL

BAKİ 2026

SUMQAYIT ŞƏHƏRİ, NOVXANI BAĞ
MASSIVI, 3873D ÜNVANINDA
YERLƏŞƏN FƏRDİ YAŞAYIŞ EVİNİN

MEMARLIQ-PLANLAŞDIRMA BÖLMƏSİ

DİREKTOR
NİGAR B.ƏSƏD

LBM
HÜSEYİNOVA M.

 PROJE44

TEL: +994103045252
E-POÇT: PPROJE44@GMAIL.COM

M.P.B markalı əsas dəstin cizgilləri cədvəli

Nö	ADI	Qeyd
1	Ümumi məlumatlar	
2	Mövqe planı	
3	Baş plan	
4	Bünövrə planı	
5	1-ci mərtəbənin planı	
6	2-ci mərtəbənin planı	
7	Kəsim 1-1	
8	Kəsim 2-2	
9	Ön Fasad	
10	Arxa Fasad	
11	Sol Fasad	
12	Sağ Fasad	
13	Dam-çardağ hissəsi	

Layihələndirilən yaşayış evi	
Texniki-iqtisadi göstəricilər	
Göstəricilərin adı	Göstərici
Tikinti ərazisi (m ²)	0.025 ha
Tikinti sahəsi (m ²)	130.2 m ²
Ümumi sahəsi (m ²)	197.5 m ²
Mərtəbənin sayı (ədəd)	2
Otaqların sayı(ədəd)	6
Bütün yerüstü mərtəbələrinin xarici divarlarla ümumi sahəsi	260.4 m ²
Binanın hündürlüyü	6.20 m
Xarici divarların hündürlüyü	6.80 m


Layihə binaların və ya qurğuların təhlükəsiz istismarını təmin edən və qüvvədə olan normalara və qanunlara əsaslanaraq işlənib.

Layihənin baş memarı

- Şərti ±0.00 səviyyəsi 1-ci mərtəbənin döşəmə səviyyəsi qəbul edilmişdir.
- Binanın konstruksiyası - yarım karkasdır. Bünövrə - lentvaridir. Karkas elementləri - zəlzələ kəməri, rigellər dəmir-betondandır.
- Xarici və daxili divarlar markası M"50"-dən az olmayan mişarlanmış əhəng daşından və M"50" markası olan sement məhlulu ilə hörülür. Daş hörgüsündə II kateqoriyalı hörgüyə olan tələblərə (Snip-7-81*) əməl olunmalıdır. Torpaqla təmasda olan hissəsi müvafiq qaydada üfüqi və şaquli hidroizolyasiya olunur.
- Xarici və daxili divarların öz aralarında və sütunlarla birləşmə yerlərində hörgünün hündürlüyü boyunca hər H-60 sm-dan bir metal tor qoyulmalıdır.
- Arakəsmələr mişar daşındann hörülür. Arakəsmələr üfüqi istiqamətdə hər 6 cərgədən bir 2f4 B1-1 markalı məftillə gücləndirilir.
- Fasadlarda 1-ci n yüksək keyfiyyətli emulsiya ilə rənglənməsi, kürsülük mərtəbəsi isə yüksək keyfiyyətli emulsiya ilə rənglənməsi nəzərdə tutulur.
- Pilləkən - daş konstruksiyası. Pilləkən məhəccərlərinin hündürlüyü 1.0mdən az olmamalıdır.
- Dam - taxta çardaq konstruksiyası.
- Damın atmosfer sularının axıdılması üçün xarici boru suaxarlar quraşdırılmalıdır.
- Ölçülər sm-ilə verilib.
- Miqyas M1:100, M1:500
- Memarlıq-planlaşdırma həlli A4 vərəqində çapdan çıxardılmalıdır.

	Sumqayıt şəhəri, Novxanı bağ massivi, 3873D			
MİQYAS 1:100	Sifarişçi: Abbasova Əfsanə Şamil qızı			
DİREKTOR NİGAR B. ƏSƏD	Fərdi yaşayış evi	Mərhələlər	Vərəq	Vərəqlər
LBM HÜSEYNOVA M.		E.L	1	13
	Ümumi məlumatlar	"PROJE44" MMC		



MÖVQE PLANI

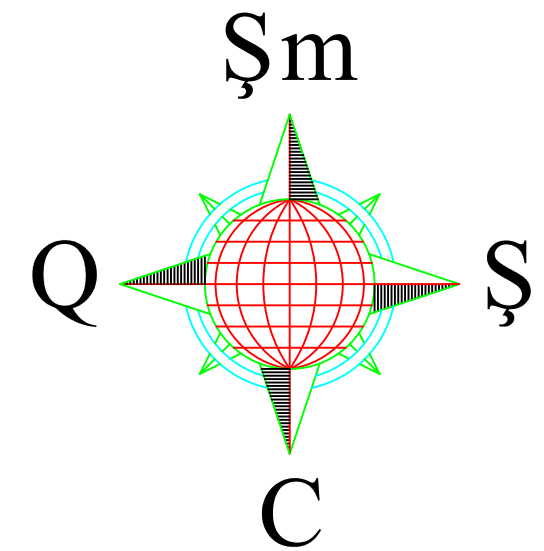

X-393455.9395	Y- 4488046.5013
X-393452.4416	Y- 4488071.1239
X-393456.4328	Y- 4488071.9808
X-393462.2592	Y- 4488073.0194
X-393465.7991	Y- 4488048.1713


		<u>Sumqayıt şəhəri, Novxanı bağ massivi,3873D</u>			
MİQYAS 1:100					
		Sifarişçi; <u>Abbasova Əfsanə Şamil qızı</u>			
Direktor Nigar B.Əsəd.		Fərdi yaşayış evi	Mərhələ	Vərəq	Vərəqlər
LBM Hüseynova M.			M.P.B	2	13
		Mövqe planı			

BAŞ PLANI

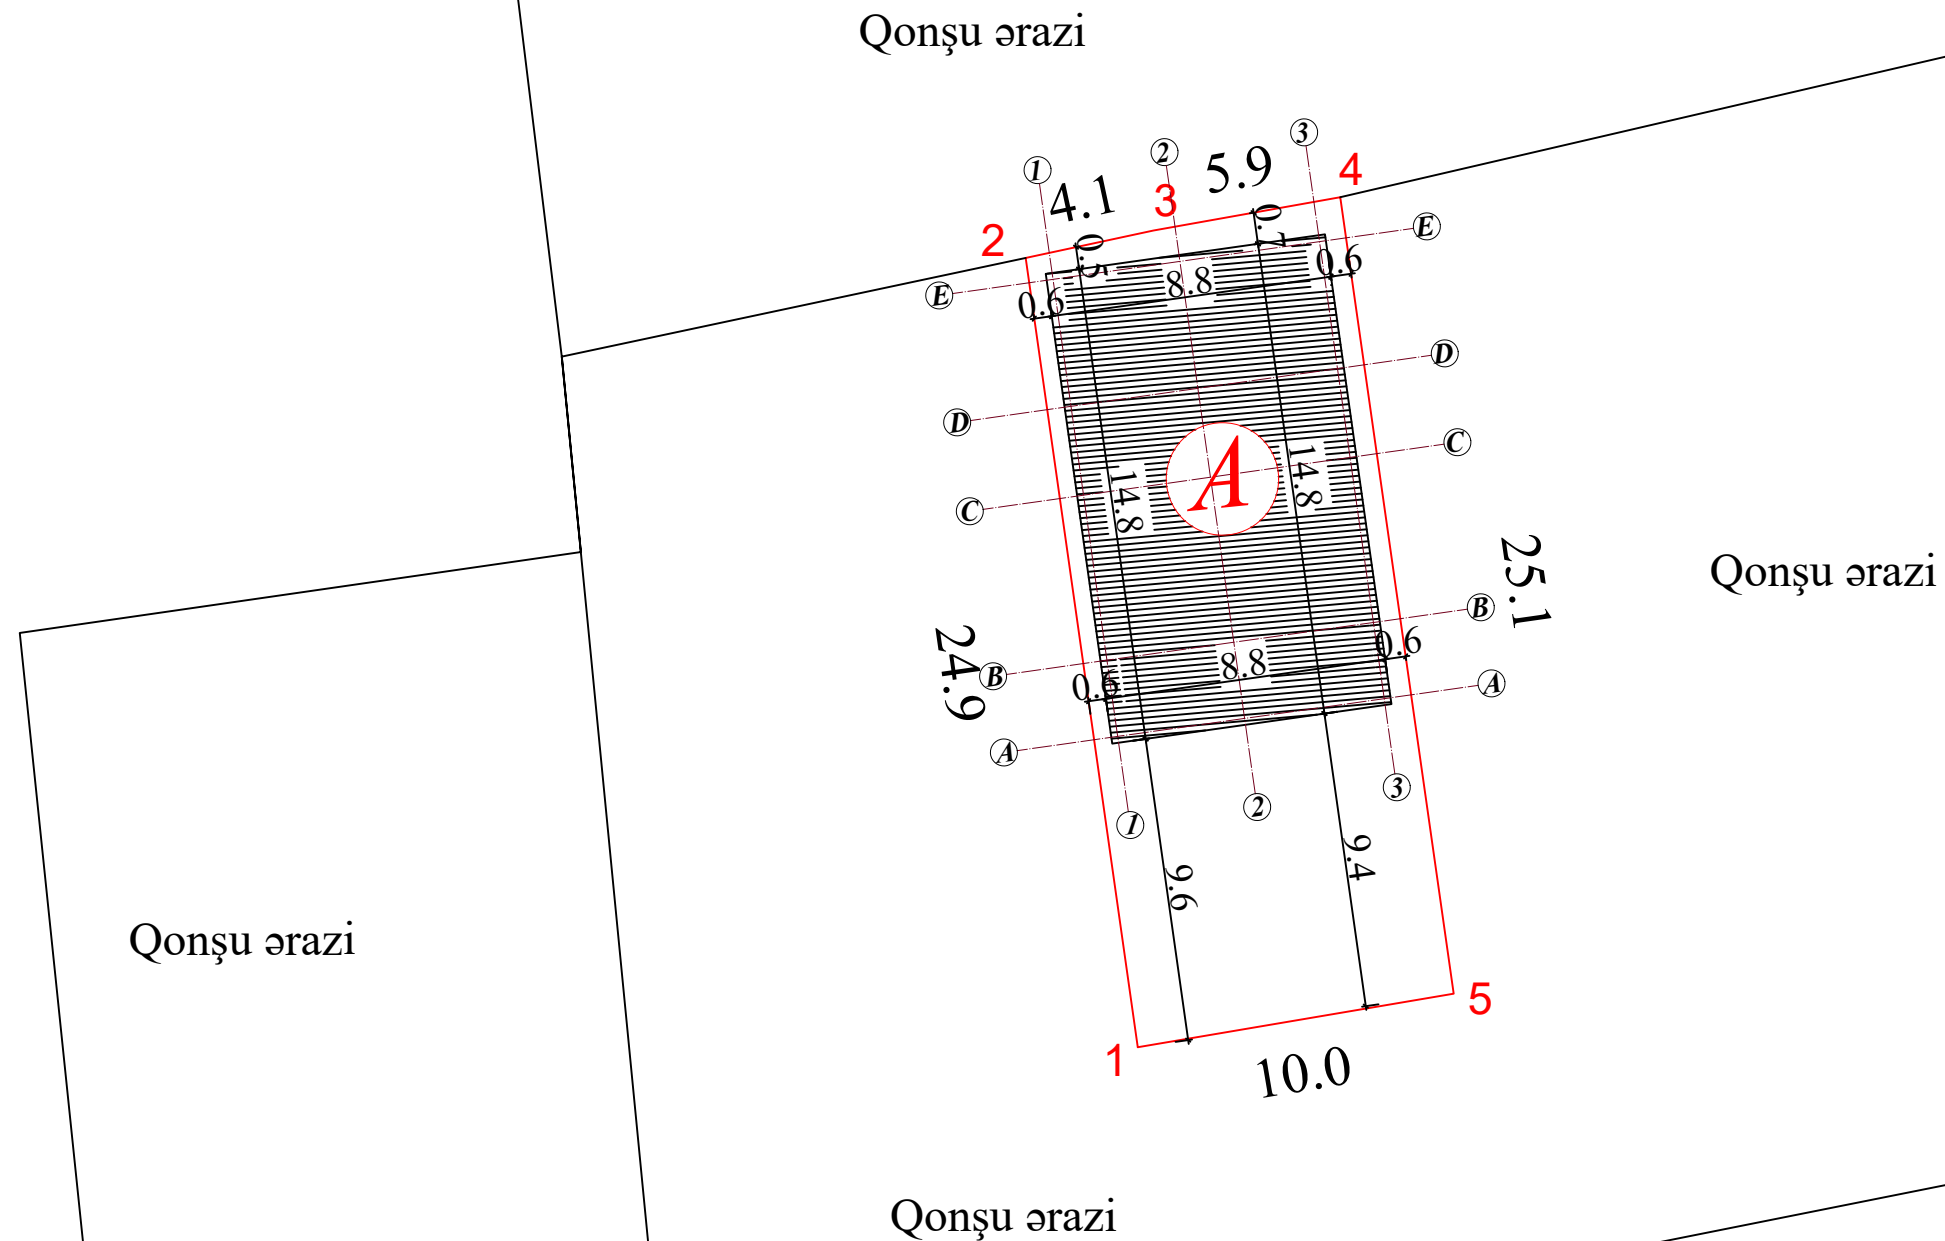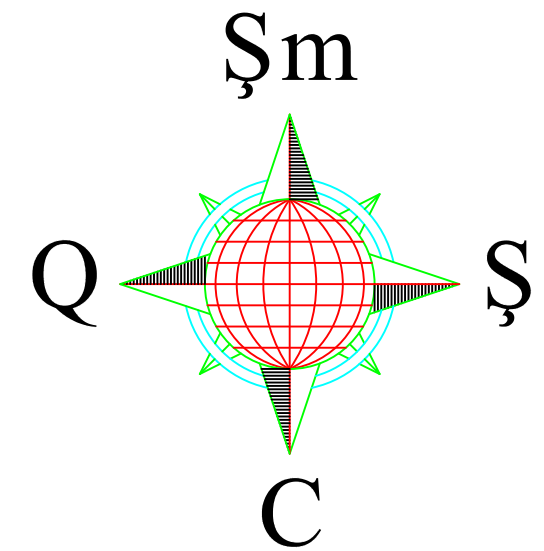


A - Layihələndirilən fərdi yaşayış evi

		<u>Sumqayıt şəhəri, Novxanı bağ massivi,3873D</u>				
MİQYAS 1:100		Sifarişçi; <u>Abbasova Əfsanə Şamil qızı</u>				
Direktor Nigar B.Əsəd.		Fərdi yaşayış evi		Mərhələ	Vərəq	Vərəqlər
LBM Hüseynova M.				M.P.B	3	13
		Baş plan				

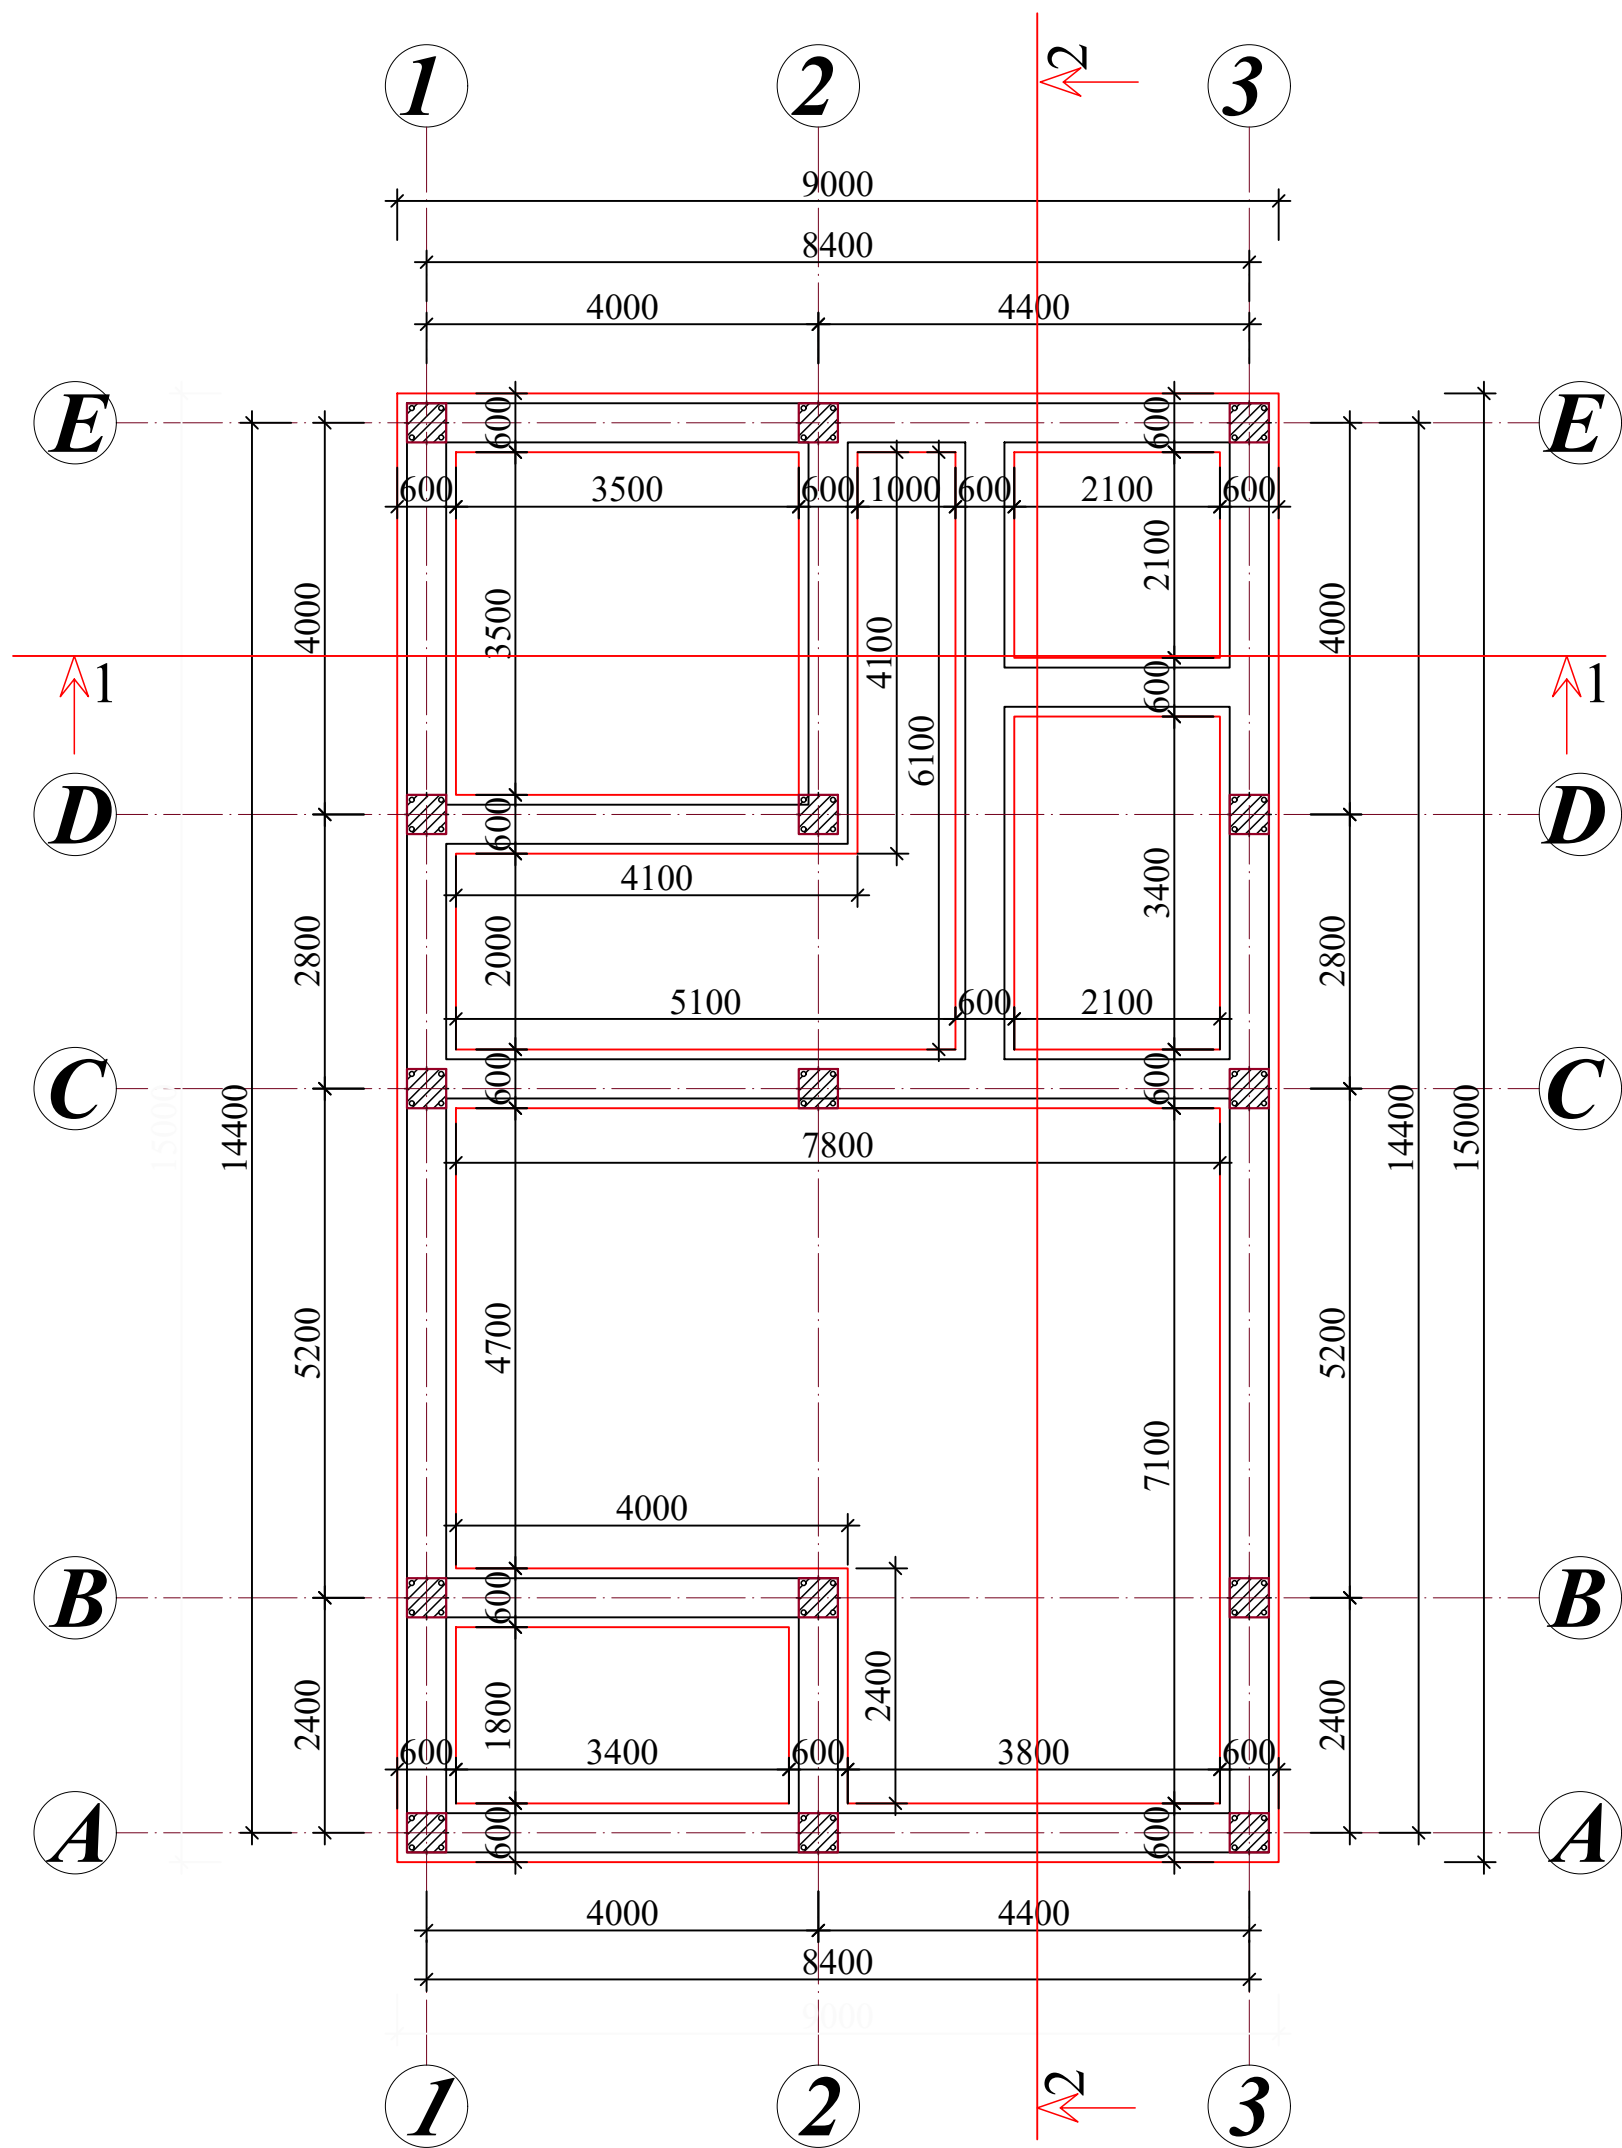


		<u>Sumqayıt şəhəri, Novxanı bağ massivi,3873D</u>			
1:100					
		Sifarişçi; <u>Abbasova Əfsanə Şamil qızı</u>			
Direktor Nigar B.Əsəd.		Fərdi yaşayış evi	Mərhələ	Vərəq	Vərəqlər
LBM Hüseynova M.			M.P.B	4	13
		1-ci mərtəbənin planı			

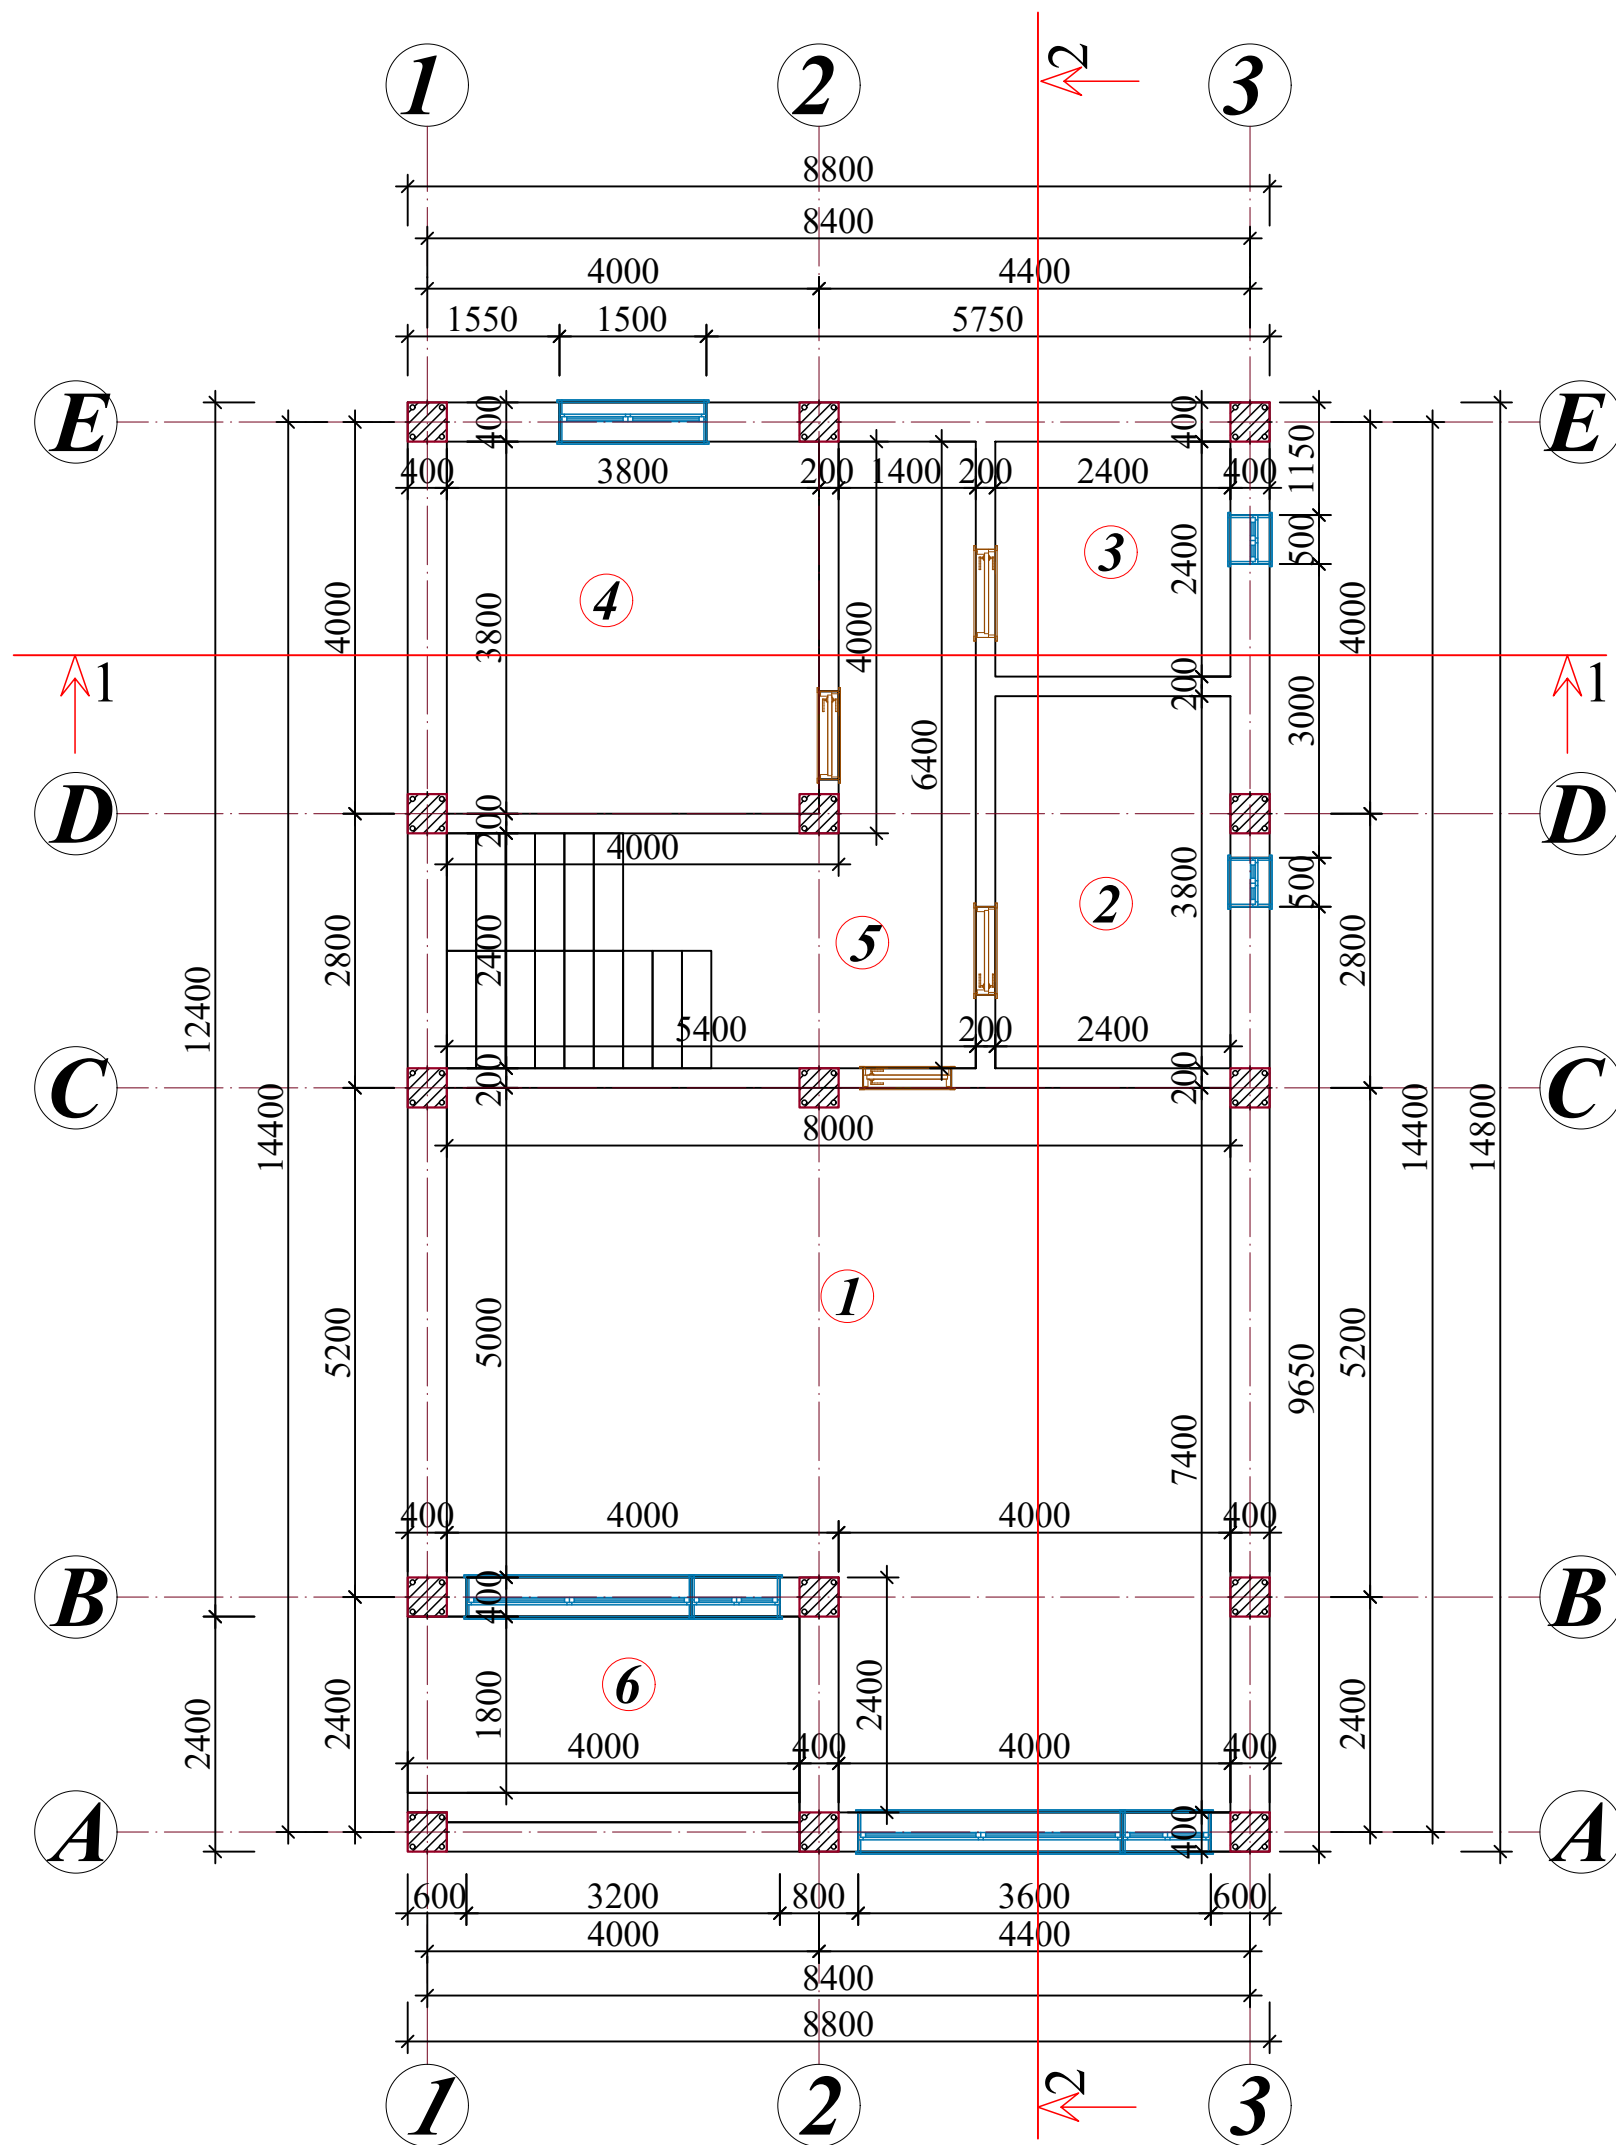

Otaqların təsnifatı

Otaqların təsnifatı		
№	ADI	Sahə m²
1	Studio Zal	49.6 m²
2	S/Q	9.1 m²
3	S/Q	5.7 m²
4	Yataq otağı	14.4 m²
5	Holl	8.9 m²
6	Eyvan	7.2 m²
	Cəmi:	94.9 m²
	Tikintialtı:	130.2 m²

		Sumqayıt şəhəri, Novxanı bağ massivi,3873D				
MİQYAS 1:100						
		Sifarişçi; <u>Abbasova Əfsanə Şamil qızı</u>				
Direktor Nigar B.Əsəd.		Fərdi yaşayış evi		Mərhələ	Vərəq	Vərəqlər
LBM Hüseynova M.	M.P.B			5	13	
		1-ci mərtəbənin planı				

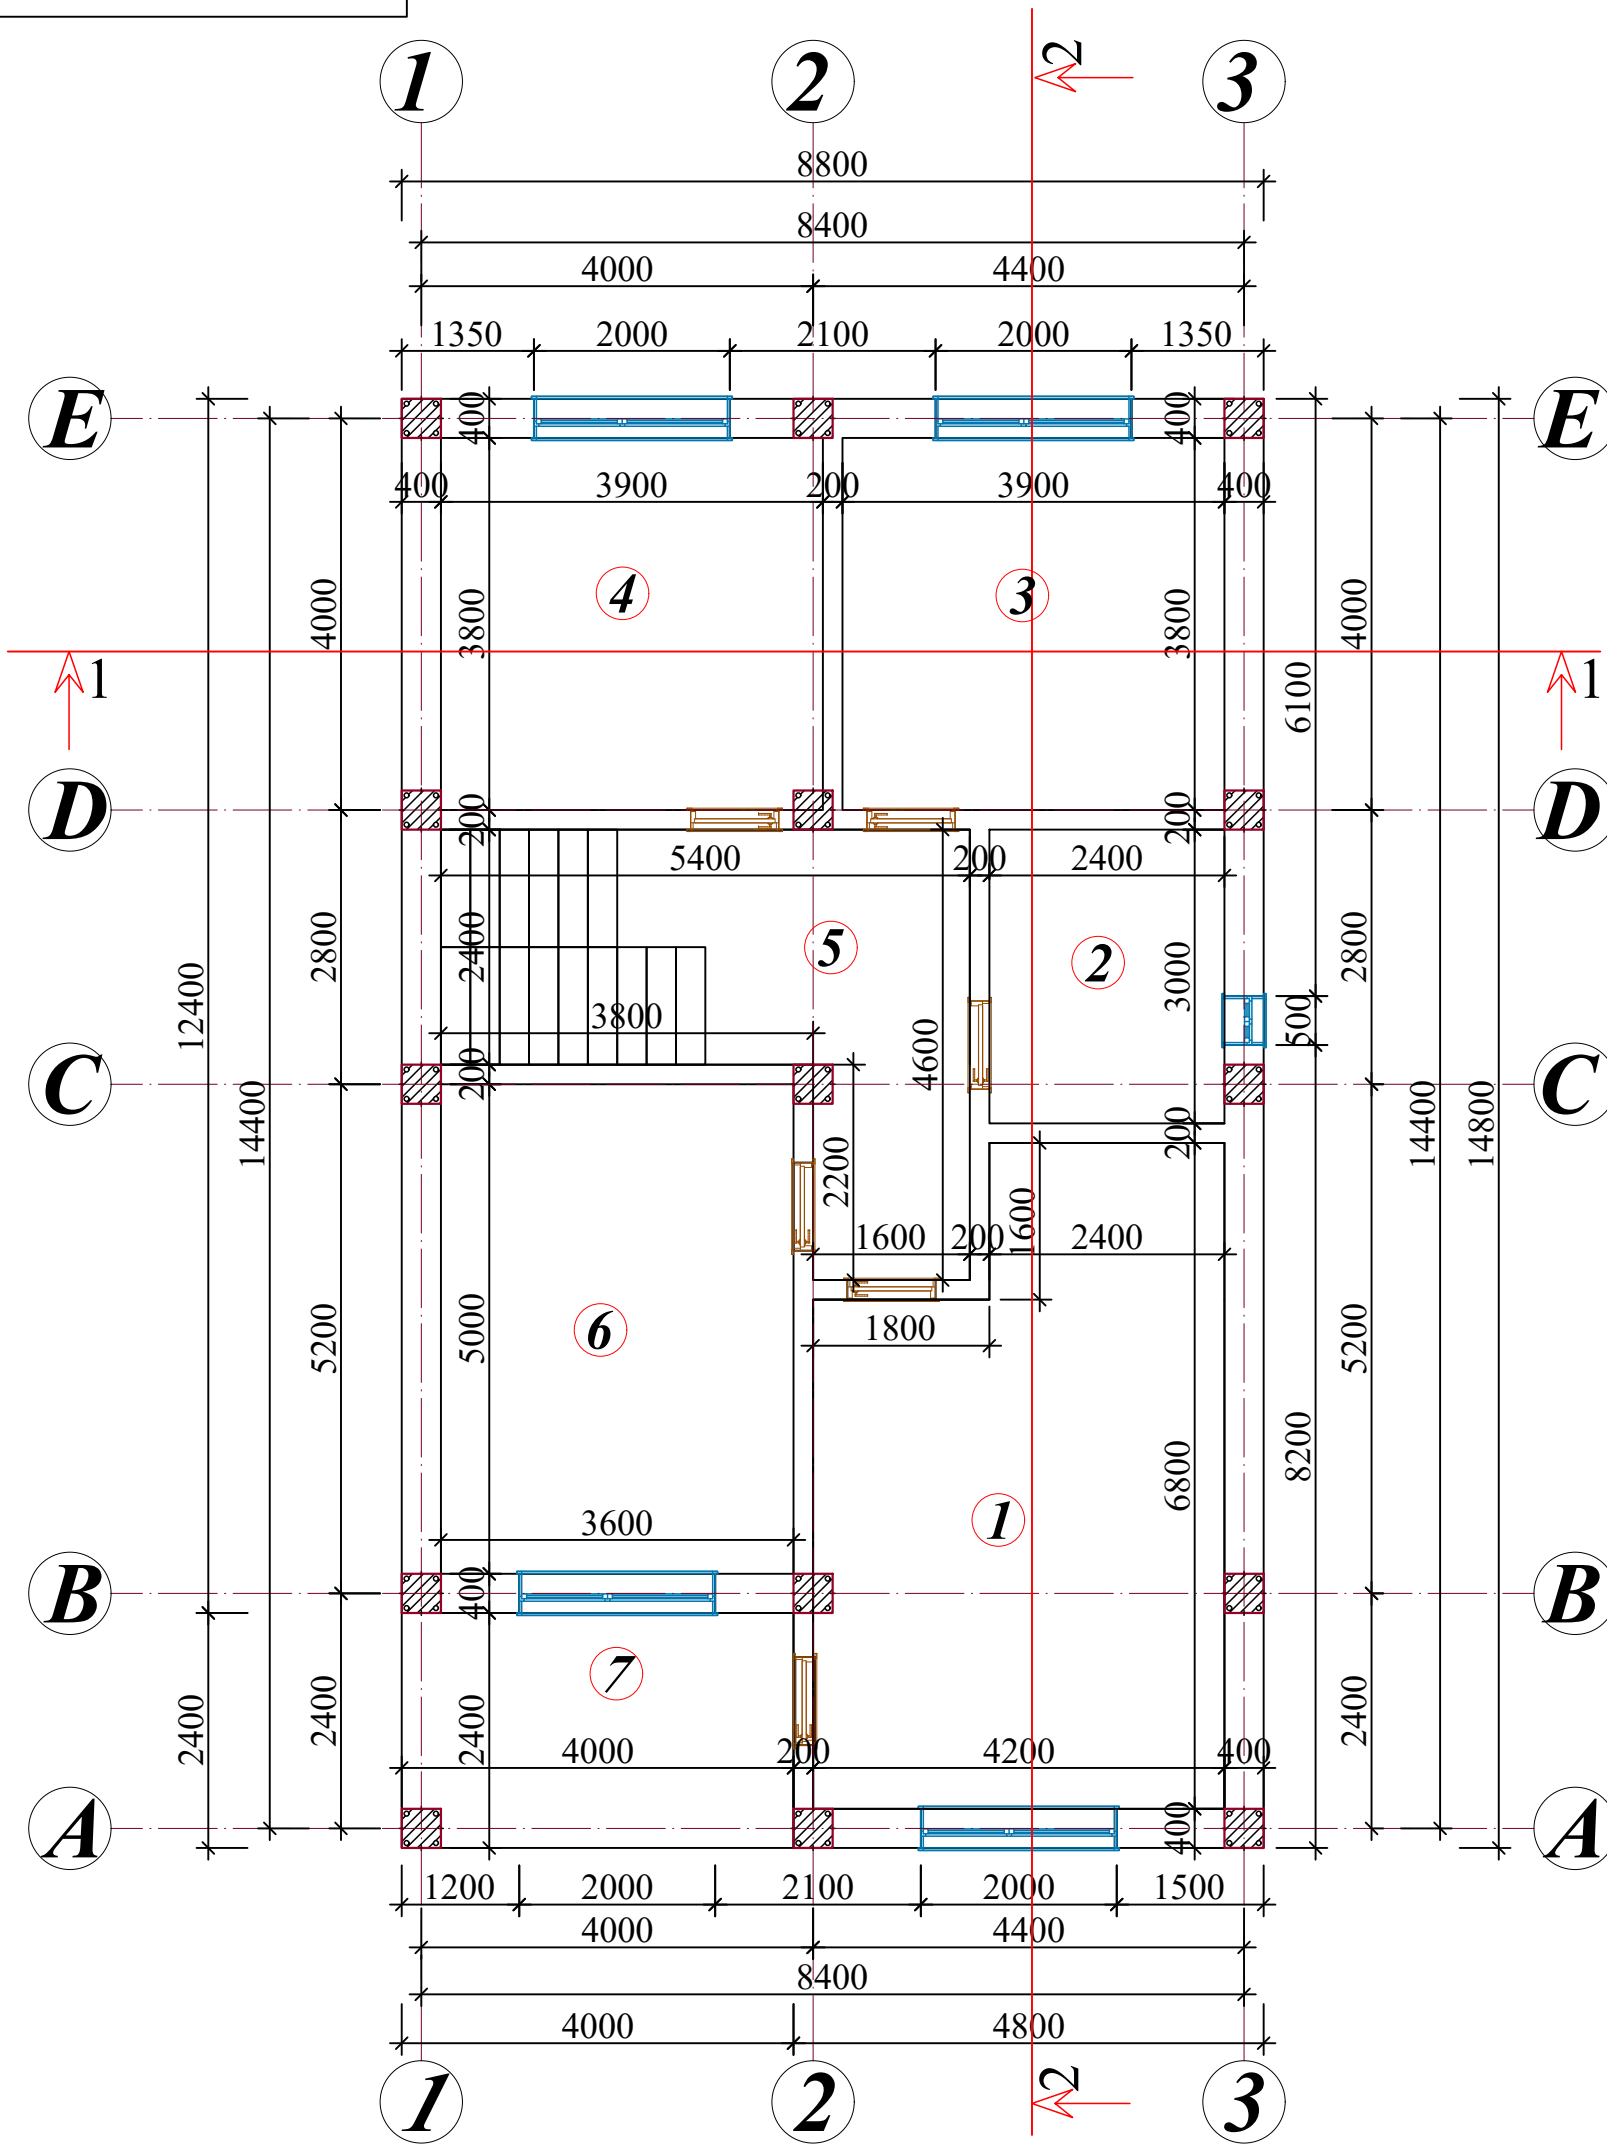

Otaqların təsnifatı

No	ADI	Sahə m²
1	Yataq otağı	21.8 m²
2	S/Q	7.2 m²
3	Yataq otağı	14.8 m²
4	Yataq otağı	14.8 m²
5	Dəhliz	16.4 m²
6	Yataq otağı	18.0 m²
7	Eyvan	9.6 m²
	Cəmi:	102.6 m²
	Tikintialtı:	130.2 m²


1:100	Sumqayıt şəhəri, Novxanı bağ massivi, 3873D
Direktor Nigar B.Əsəd.	Sifarişçi: Abbasova Əfsanə Şamil qızı
LBM Hüseynova M.	Fərdi yaşayış evi
	Mərhələ M.P.B
	Vərəq 6
	Vərəqlər 13
	2-ci mərtəbənin planı
	PROJE44

KƏSİM 1-1


Metal kirəmit

Qabırğa 50x50 ad.350

Çatqı ayağı

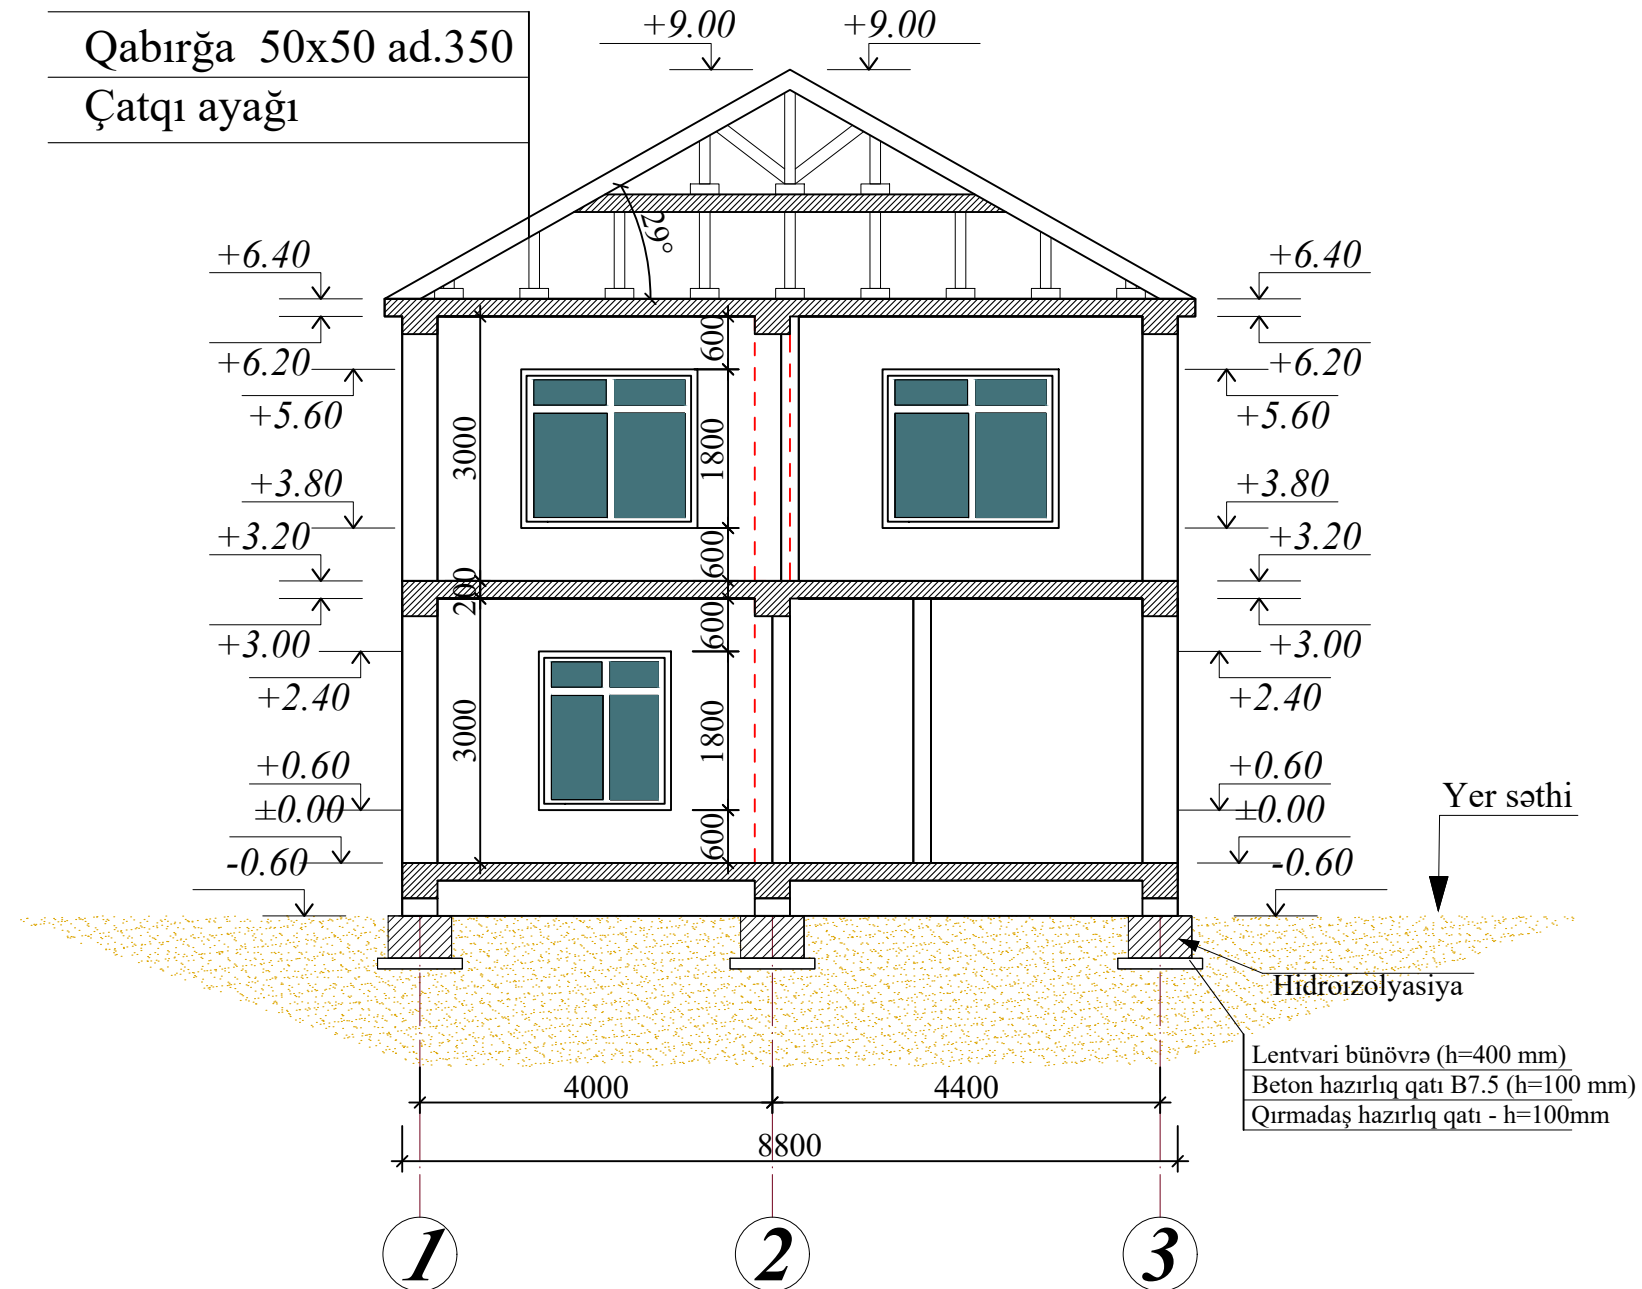

-
1. Keramik tavalar (sürüşməyən)-13mm
 2. "150"markalı sement-qum məhlulu-15mm
 3. "150"markalı sement-qum məhlulu-40mm
 4. Səsizolyasiya qatı-qum -32mm
 5. Monolit dəmir-beton örtük tavası

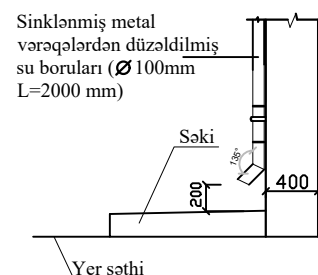


-
1. Taxta -29mm
 2. Laqa taxta 100x40(h)
 3. Taxtalıflı səsuducu qat, M-2 və M-3 markalı -31mm

		<u>Sumqayıt şəhəri, Novxanı bağ massivi,3873D</u>			
MİQYAS 1:100					
		Sifarişçi; <u>Abbasova Əfsanə Şamil qızı</u>			
Direktor Nigar B.Əsəd.		Fərdi yaşayış evi	Mərhələ	Vərəq	Vərəqlər
LBM Hüseynova M.			M.P.B	7	13
		Kəsim 1-1			


Metal kirəmit

Qabırğa 50x50 ad.350

Çatqı ayağı

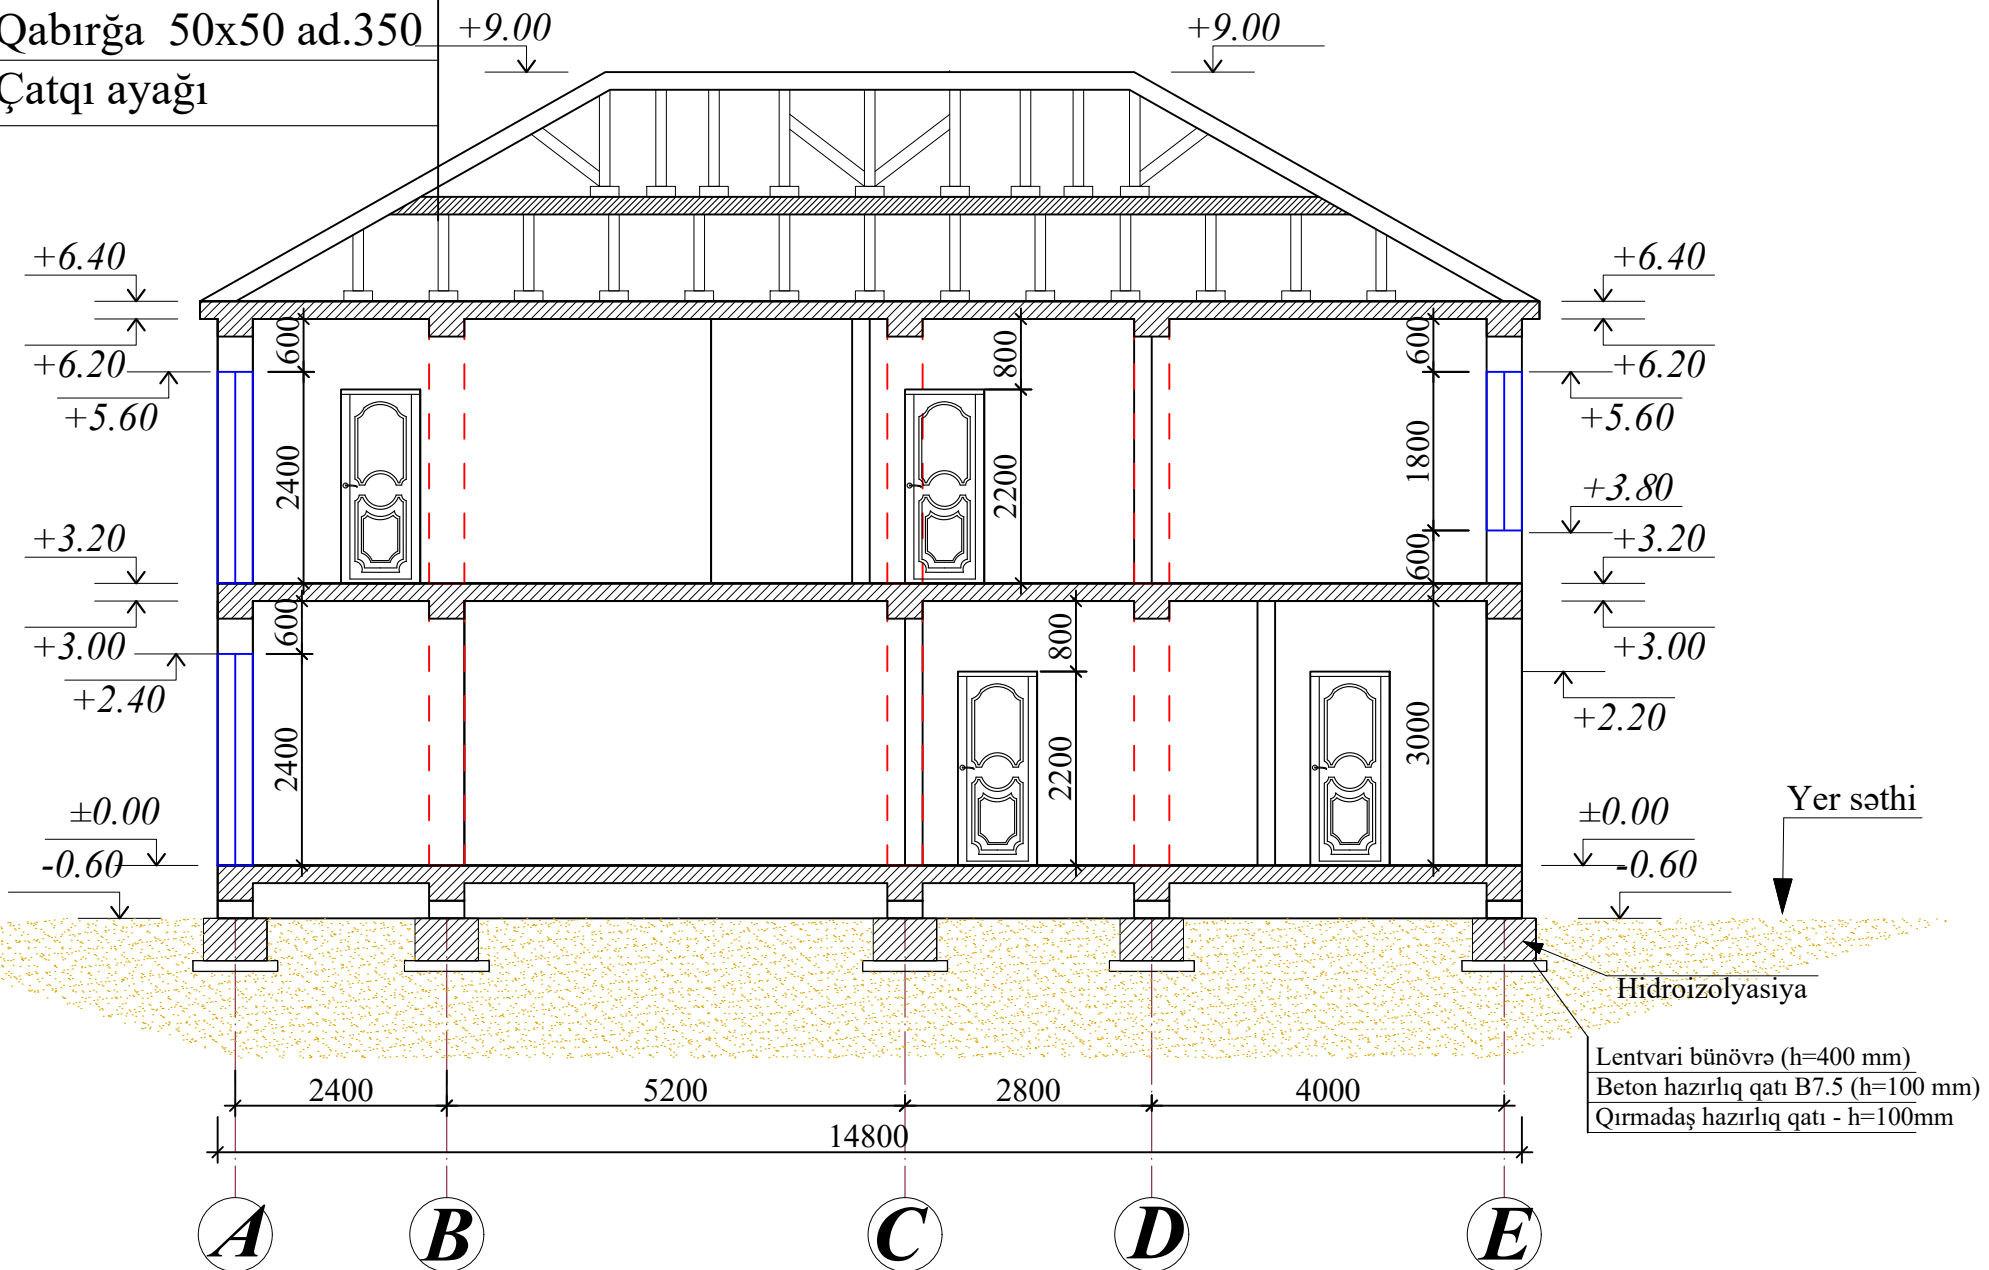


- 1.Keramik tavalar (sürüşməyən)-13mm
- 2."150"markalı sement-qum məhlulu-15mm
- 3."150"markalı sement-qum məhlulu-40mm
- 4.Səsizolyasiya qatı-qum -32mm
- 5.Monolit dəmir-beton örtük tavası

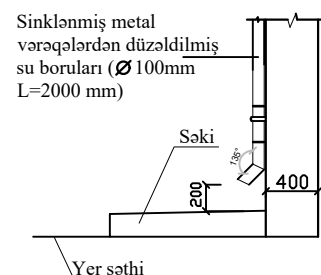

- 1.Taxta -29mm
- 2.Laqa taxta 100x40(h)
- 3.Taxtalıfli səsuducu qat,M-2 və M-3 markalı -31mm


		<u>Sumqayıt şəhəri, Novxanı bağ massivi,3873D</u>			
MİQYAS 1:100					
		Sifarişçi; <u>Abbasova Əfsanə Şamil qızı</u>			
Direktor Nigar B.Əsəd.					
LBM Hüseynova M.		Fərdi yaşayış evi	Mərhələ	Vərəq	Vərəqlər
			M.P.B	8	13
		KƏSİM 2-2			

ÖN FASAD

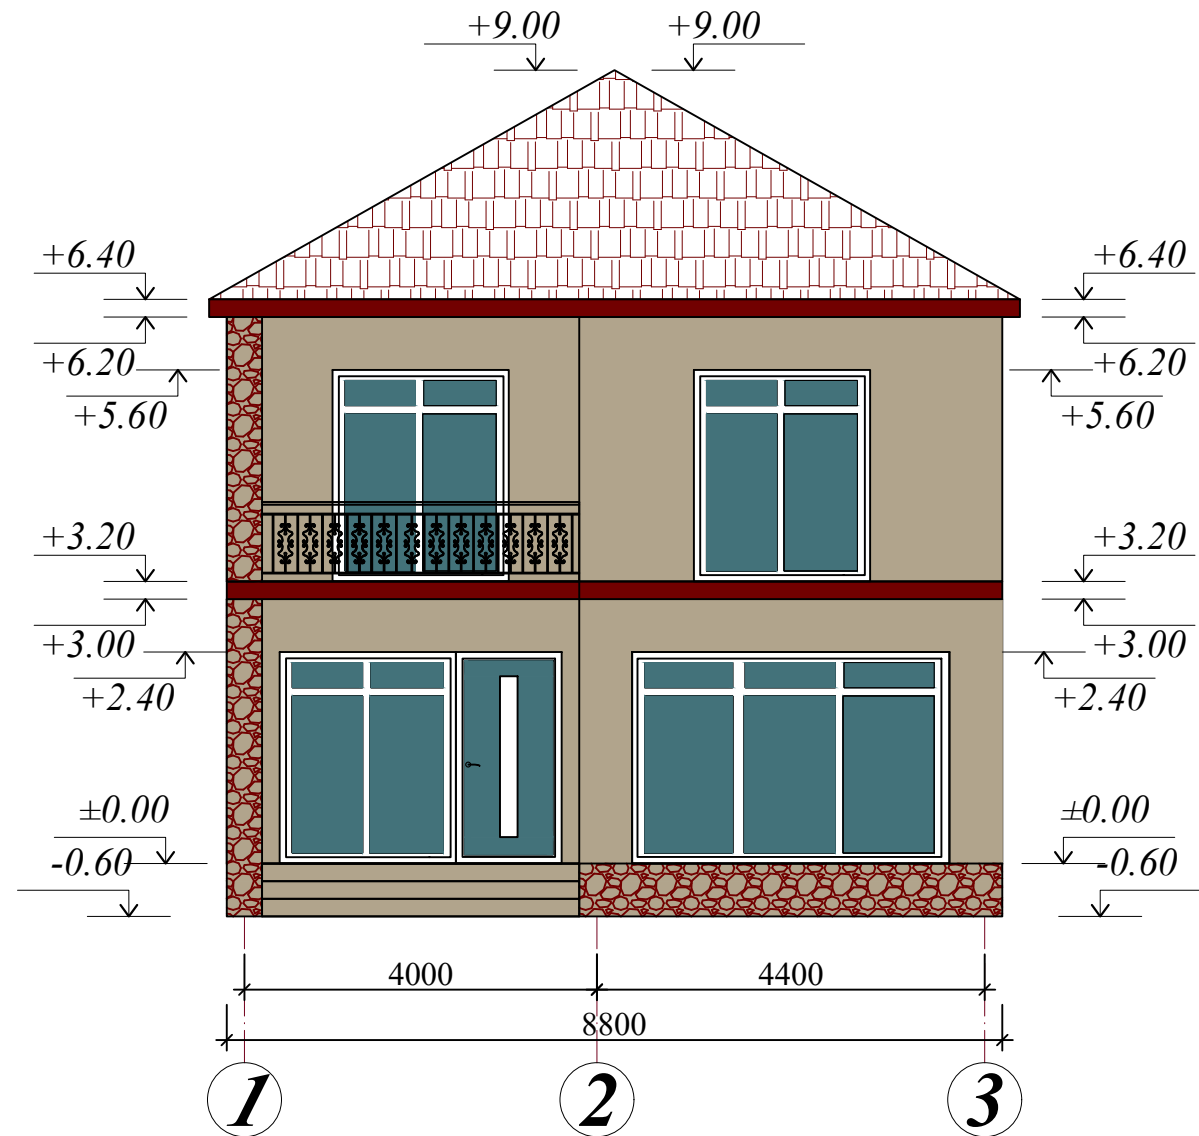


		<u>Sumqayıt şəhəri, Novxanı bağ massivi,3873D</u>			
MİQYAS 1:100					
		Sifarişçi; <u>Abbasova Əfsanə Şamil qızı</u>			
Direktor Nigar B.Əsəd.		Fərdi yaşayış evi	Mərhələ	Vərəq	Vərəqlər
LBM Hüseynova M.			M.P.B	9	13
		Ön Fasad			

ARXA FASAD

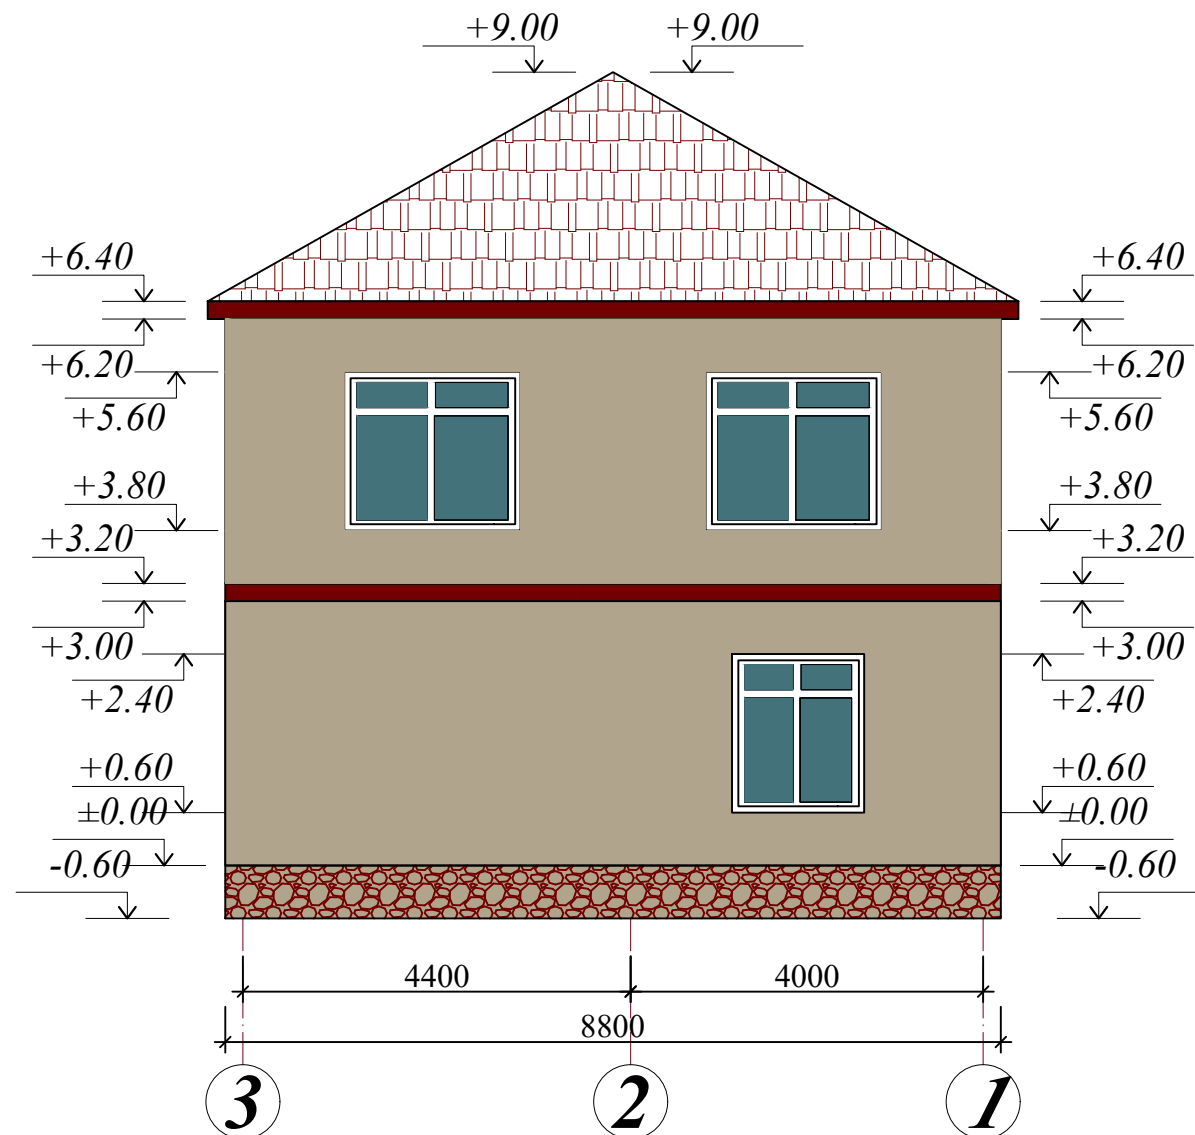


		Sumqayıt şəhəri, Novxanı bağ massivi,3873D			
MİQYAS	1:100	Sifarişçi; <u>Abbasova Əfsanə Şamil qızı</u>			
Direktor	Nigar B.Əsəd.	Fərdi yaşayış evi	Mərhələ	Vərəq	Vərəqlər
LBM	Hüseynova M.		M.P.B	10	13
		Arxa Fasad			

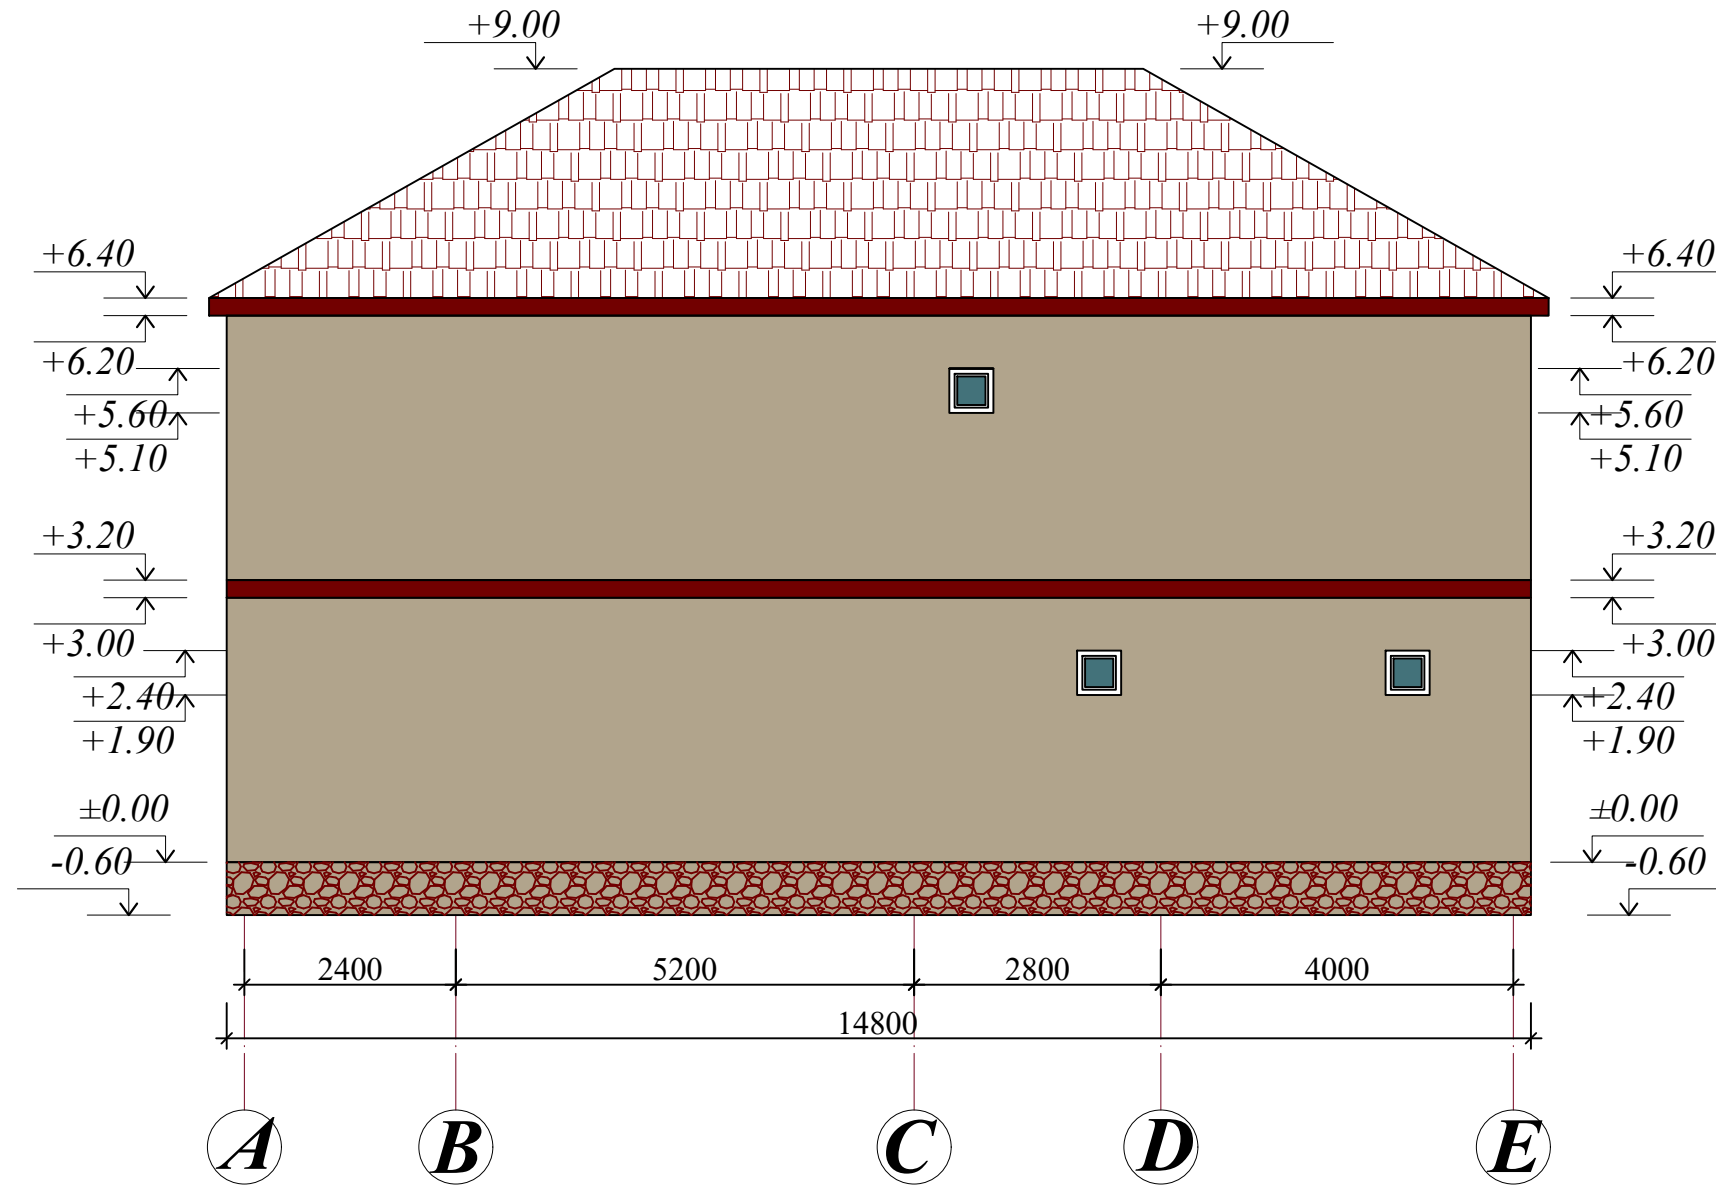


		Sumqayıt şəhəri, Novxanı bağ massivi,3873D		
MİQYAS	1:100	Sifarişçi; Abbasova Əfsanə Şamil qızı		
Direktor	Nigar B.Əsəd.	Fərdi yaşayış evi	Mərhələ	Vərəq
LBM	Hüseynova M.		M.P.B	Vərəqlər
		Sol Fasad	11	13
			PROJE44	

SAĞ FASAD

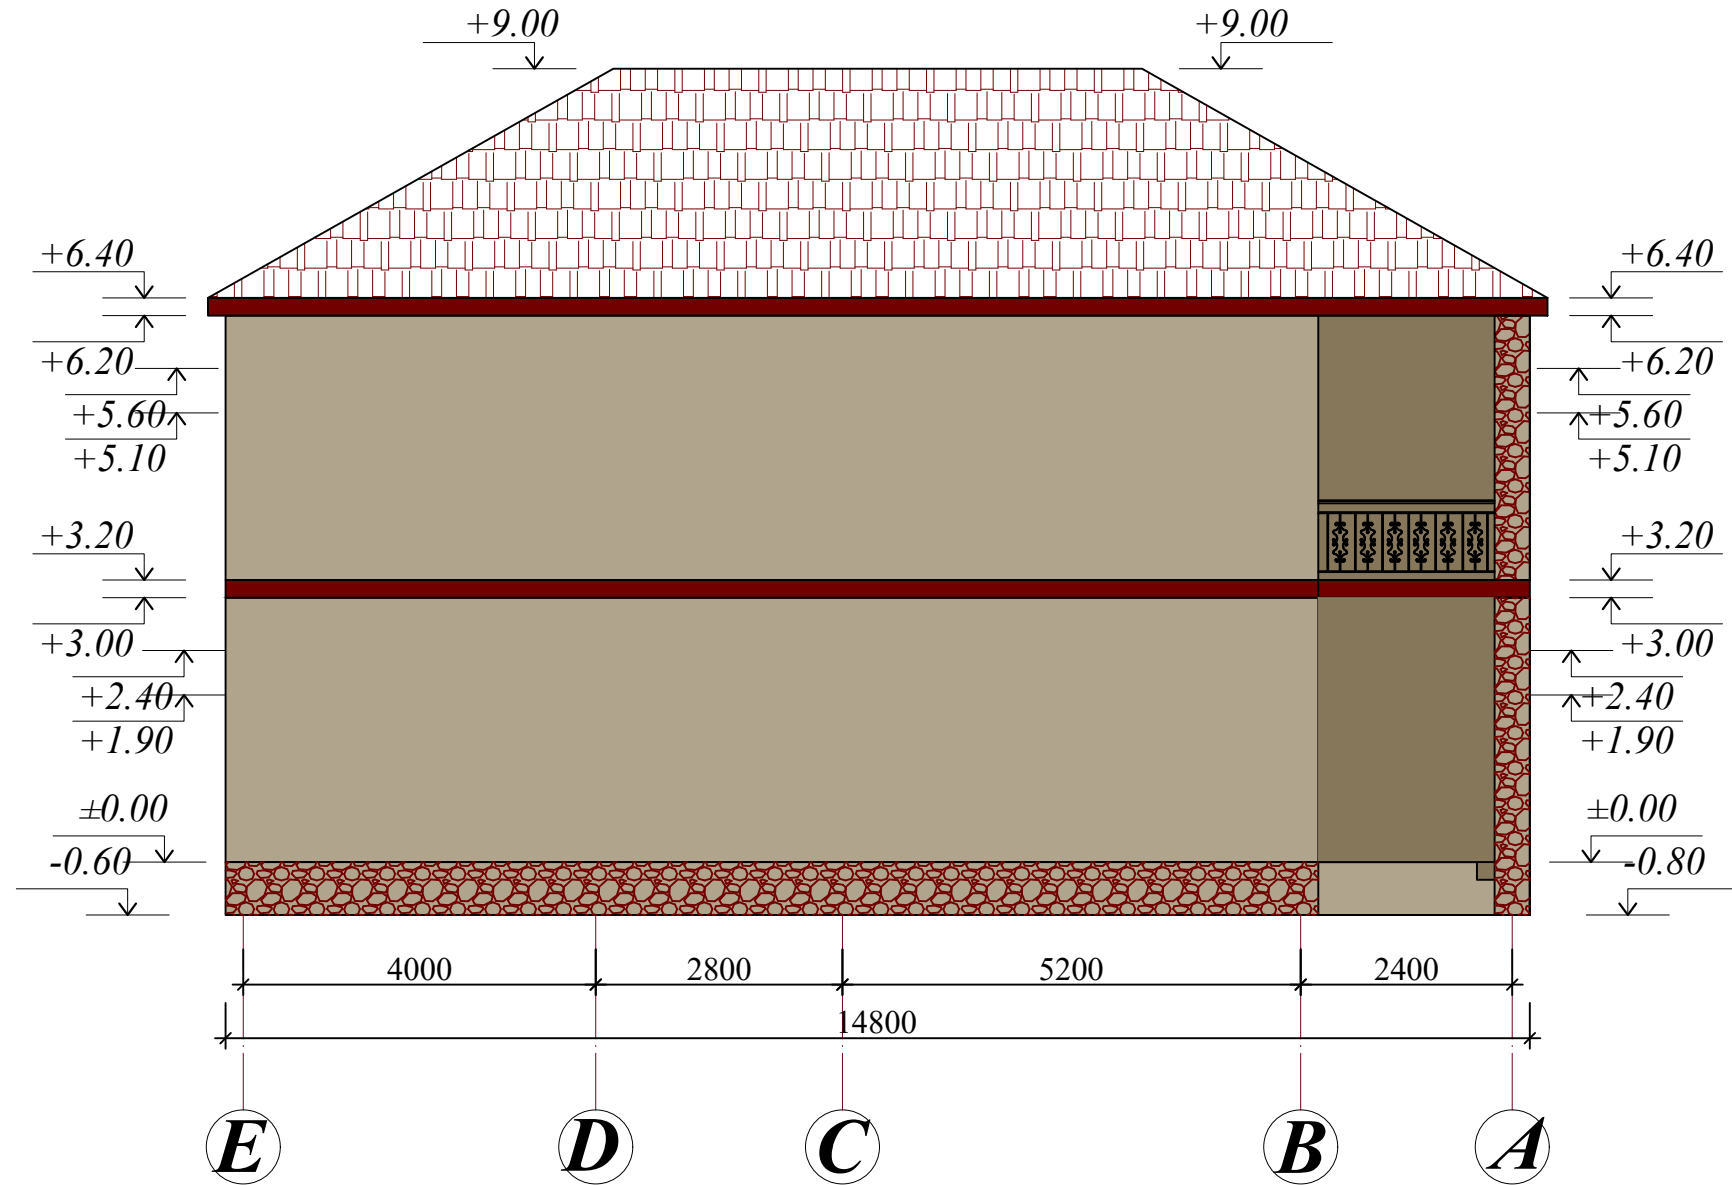

		Sumqayıt şəhəri, Novxanı bağ massivi, 3873D			
MİQYAS 1:100		Sifarişçi; Abbasova Əfsanə Şamil qızı			
Direktor Nigar B.Əsəd.		Fərdi yaşayış evi	Mərhələ	Vərəq	Vərəqlər
LBM Hüseynova M.			M.P.B	12	13
		Sağ Fasad		PROJE44	

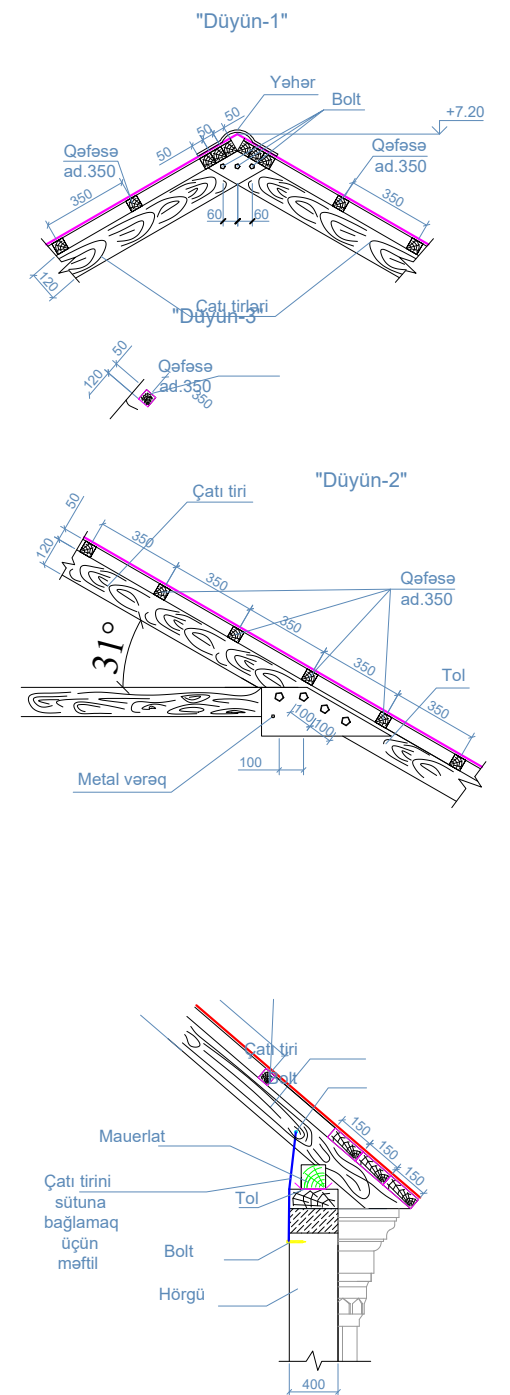

		Sumqayıt şəhəri, Novxanı bağ massivi,3873D			
MİQYAS 1:100		Sifarişçi; <u>Abbasova Əfsanə Şamil qızı</u>			
Direktor Nigar B.Əsəd.		Fərdi yaşayış evi	Mərhələ	Vərəq	Vərəqlər
LBM Hüseynova M.			M.P.B	13	13
		Dam-çardaq hissəsi			